8602050314 Vol 309 Pg 1253

ON-SITE DISPOSAL SYSTEM AND PRESSURE LINE EASEMENT

THIS INDENTURE WITNESSETH: Heller Financial, Inc., the owner of the property hereinafter described, for and in consideration of the sum of One Dollar ($1.00) and other good and valuable consideration to him in hand paid by Springfield Waste Mgmt. Assn., the receipt of which is hereby acknowledged, has and does hereby grant unto Springfield Waste Mgmt. Assn. the perpectual right and privilege to construct and maintain a sewer pressure line and on-site disposal system over, under, along and across the following described real property in Pierce County, Washington, to-wit:

The East 5.0' of Lot 226; the East 5.0' of Lot 227; the East 5.0' of Lot 228; the North 15' of Lot 229; the South 10' of Lot 230; the South 10' of the West 10' of Lot 246; the West 10' of Lot 247; the West 12' of Lot 248; the West 10' of Lot 249; the West 5.0' of Lot 250; the West 5.0' of Lot 251; the West 5.0' of Lot 252; the East 10.0' of the South 30.0' of revised Lot 254 as shown on the Declaration of Boundary Line Revision as recorded under Auditor's Fee No. 8602040329, records of Pierce County. The North 6.0' of Lot 255; the Northerly 15.0' of Lots 259, 260, 261 and 262 and the West 15.0' of Lot 263.

All in the Plat of Springfield as recorded under Auditor's Fee No. 8011260320, records of Pierce County.

86 FEB 5 P 3:17
RICHARD A. GALE AUDITOR
PIERCE COUNTY WASH
COUNTY

The Grantor s shall build no permanent structures within said easement.

The covenants herein contained shall run with the land and are binding upon all subsequent owners thereof.

IN WITNESS WHEREOF, Heller Financial, Inc have hereunto subscribed their name(s) at Bellevue, Washington, this 16th day of January, 1986.

WITNESS — Heller Financial, Inc
NAME

WITNESS — VP
NAME

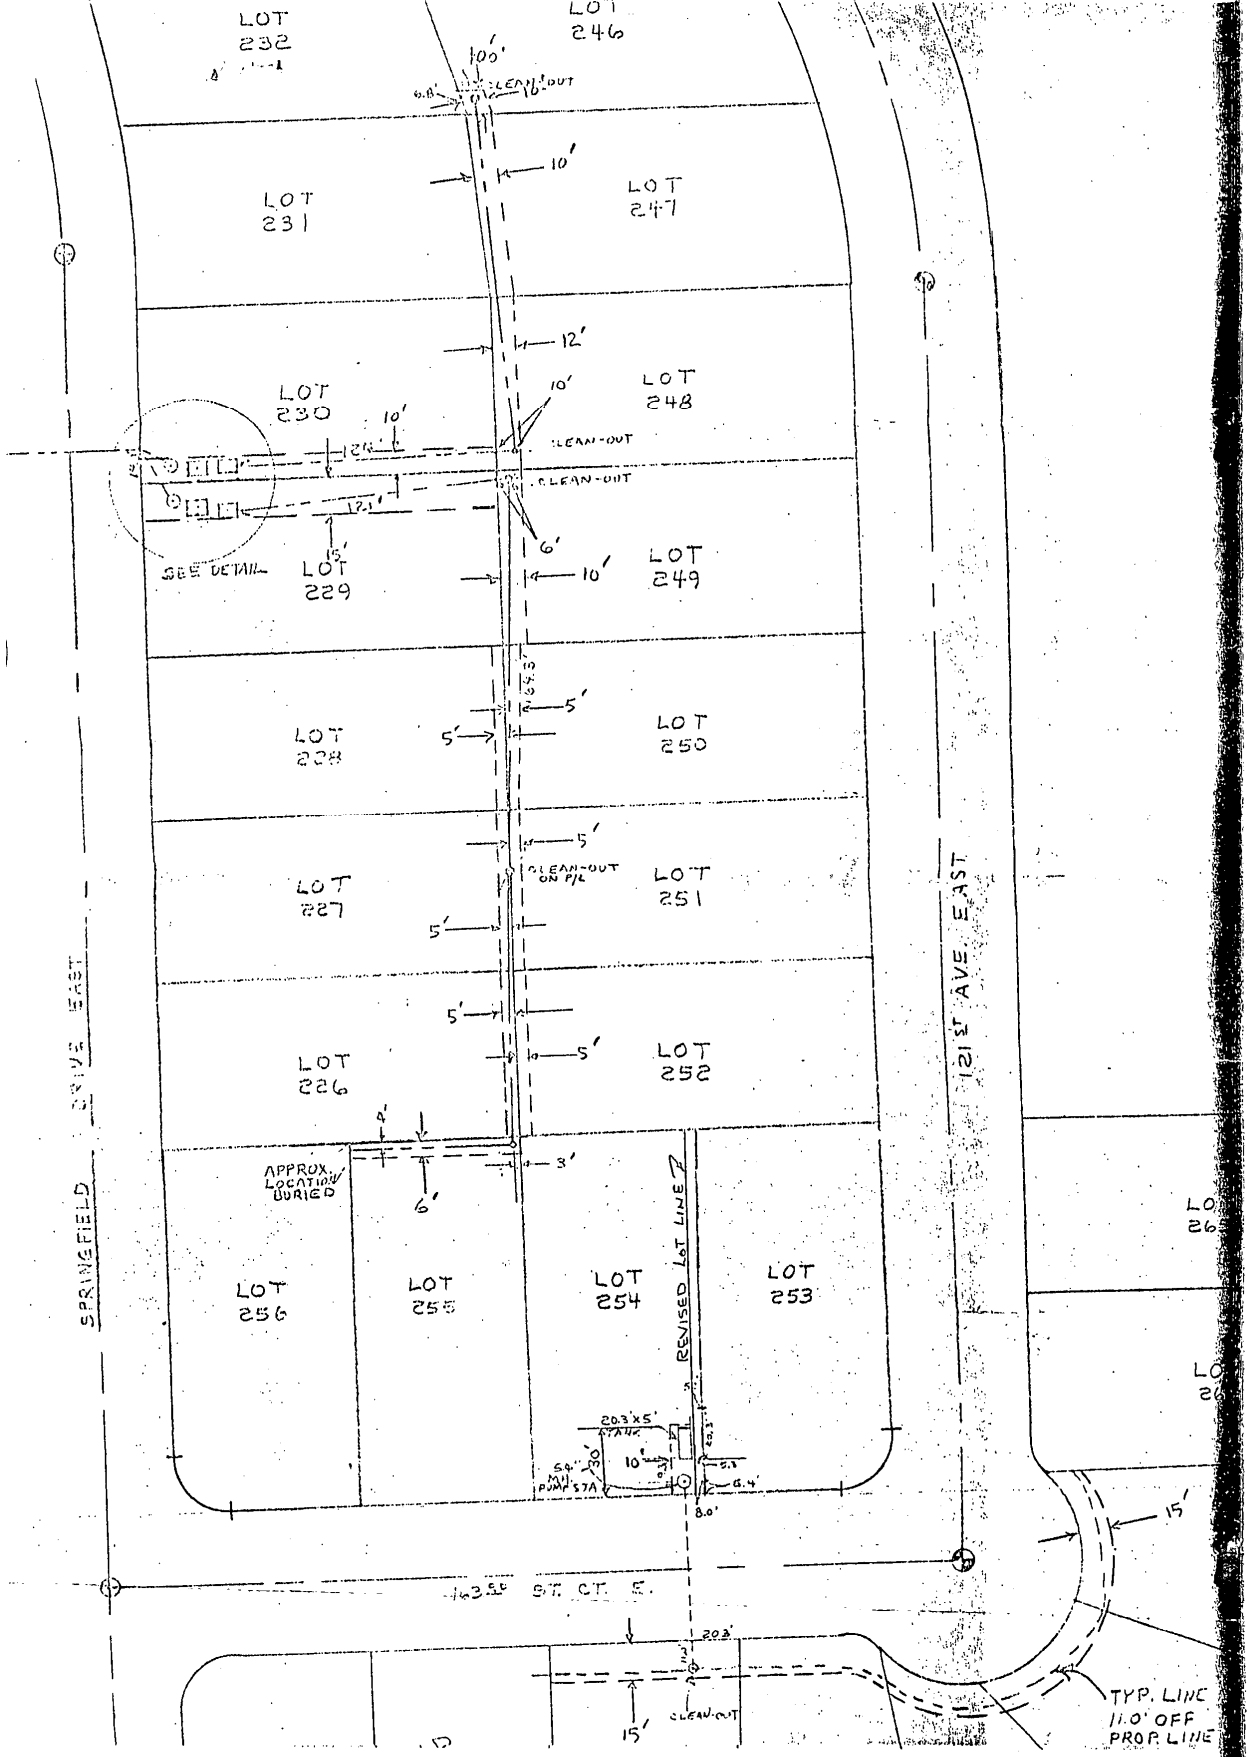
STATE OF WASHINGTON)
) ss.
COUNTY OF KING)

On this 16th day of January 1986, before me personally appeared Paul C. Chapman, to me known to be the Vice President of Heller Financial, Inc., the corporation that executed the within and foregoing instrument, and acknowledged the said instrument to be the free and voluntary act and deed of said corporation for the uses and purposes therein mentioned, and on oath stated that he was authorized to execute said instrument.

IN WITHNESS WHEREOF, I have hereunto set my hand and affixed my official seal the day and year first above written.

Sarah J Zank
NOTARY PUBLIC in and for the State of Washington, residing at Bellevue

5


LOT 232
LOT 246
LOT 231
LOT 247
LOT 230
LOT 248
LOT 229
LOT 249
LOT 228
LOT 250
LOT 227
LOT 251
LOT 226
LOT 252
LOT 256
LOT 255
LOT 254
LOT 253
SEE DETAIL
CLEAN-OUT
APPROX. LOCATION BURIED
REVISED LOT LINE
SPRINGFIELD DRIVE EAST
121ST AVE. EAST
143RD ST. CT. E.
TYP. LINE 11.0' OFF PROP. LINE